

TIMBER HILL

IN D.L.C. No's. 64 & 65
T.11S., R.5W., WB&M
BENTON COUNTY, OREGON
JUNE 1969 1" = 100'

SURVEYOR'S AFFIDAVIT
STATE OF OREGON
COUNTY OF BENTON) ss


I, Nicholas A. Yinger, Registered Professional Land Surveyor in the State of Oregon, hereby depose and say that during May, 1969 I accurately surveyed, subdivided and plotted into lots and streets the lands represented on the attached map of TIMBER HILL, the boundary of which is described as follows:

Beginning at the initial point, a 2"x36" galvanized iron pipe, which is corner of the James L. Mulkey D.L.C. No. 65
thence N 00° 18' 48" E 167.45 feet
thence N 89° 41' 13" W 117.61 feet
thence along a 75.00 foot radius curve right (the long chord of which bears N 06° 57' 25" E 25.06 feet) 25.17 feet
thence N 16° 34' 21" E 78.37 feet
thence N 04° 53' 58" E 50.56 feet
thence N 12° 14' 42" E 111.11 feet
thence N 22° 47' 13" E 50.00 feet
thence N 13° 16' 47" E 97.95 feet
thence N 56° 29' 38" E 10.00 feet
thence N 06° 29' 12" E 80.00 feet
thence N 22° 40' 32" E 78.60 feet
thence N 01° 14' 22" E 41.89 feet
thence along a 612.86 foot radius curve left (the long chord of which bears S 87° 20' 52" E 29.57 feet) 29.57 feet
thence S 88° 43' 48" E 6.95 feet
thence N 01° 16' 12" E 80.00 feet
thence along a 3432.47 foot radius curve left (the long chord of which bears S 89° 36' 00" E 104.55 feet) 104.55 feet
thence N 00° 28' 31" W 200.10 feet
thence N 04° 04' 11" E 112.72 feet
thence N 06° 37' 51" W 216.44 feet
thence N 89° 11' 51" E 357.04 feet
thence S 89° 32' 16" E 143.02 feet
thence S 22° 37' 12" E 450.46 feet
thence S 43° 06' 53" E 93.71 feet
thence S 30° 23' 29" E 86.77 feet
thence S 35° 14' 27" E 415.91 feet
thence S 16° 51' 31" E 106.69 feet
thence S 04° 38' 45" E 28.64 feet
thence S 05° 29' 52" W 100.00 feet
thence S 21° 16' 49" W 100.00 feet
thence S 38° 29' 28" W 260.48 feet
thence S 05° 57' 15" E 20.00 feet to a point on the northerly right-of-way line of Walnut Boulevard
thence along a 2261.83 foot radius curve right (the long chord of which bears S 89° 00' 16" W 75.66 feet) 75.66 feet
thence S 89° 47' 56" W 367.89 feet
thence N 89° 41' 12" W 572.80 feet to a point on the northerly right-of-way line of said Walnut Boulevard
thence N 00° 18' 47" E 200.00 feet to the point of beginning.

I further depose and say that the attached map is a true and correct representation of the lots and streets as stated on the ground with 5/8"x30" steel rods at all lot corners and points of curvature.



Subscribed and sworn before me this 24 day of May 1969
David P. Yinger
Notary Public for the State of Oregon
My commission expires November 2, 1970

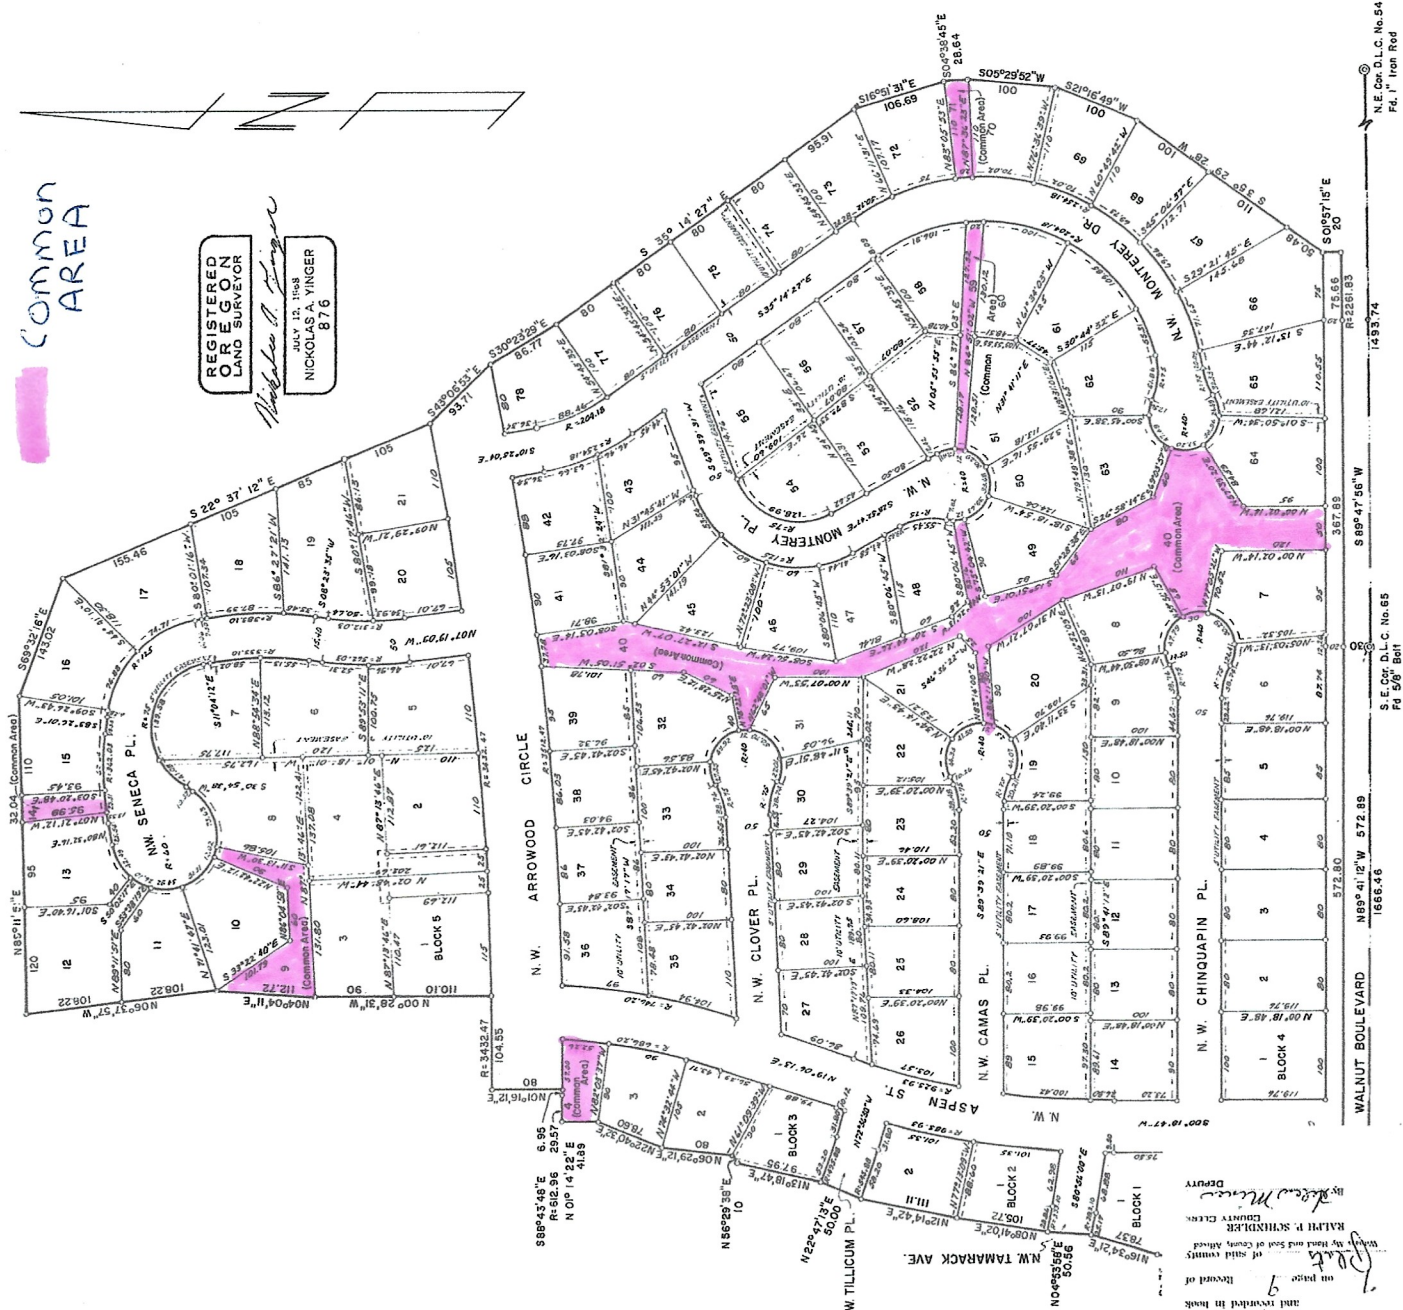

Common AREA

REGISTERED
OREGON
LAND SURVEYOR
JULY 12, 1968
NICKOLAS A. YINGER
876

on page 9
of said county
of said county
County Clerk
RALPH P. SCHINDLER
Deputy
and recorded in book


N.E. Cor. D.L.C. No. 54
Pt. 1" Iron Rod

S.E. Cor. D.L.C. No. 65
Pt. 5/8" Bolt

TIMBER HILL FIRST ADDITION
IN D.L.C. No. 64 and SEC. 22
T.I.S., R. 5W., WB&M
BENTON COUNTY, OREGON
JUNE 1969
1" = 100'

Common
 AREA

REGISTERED
 OREGON
 LAND SURVEYOR
Nickolas A. Yinger
 MAY 12, 1963
 NICKOLAS A. YINGER
 876

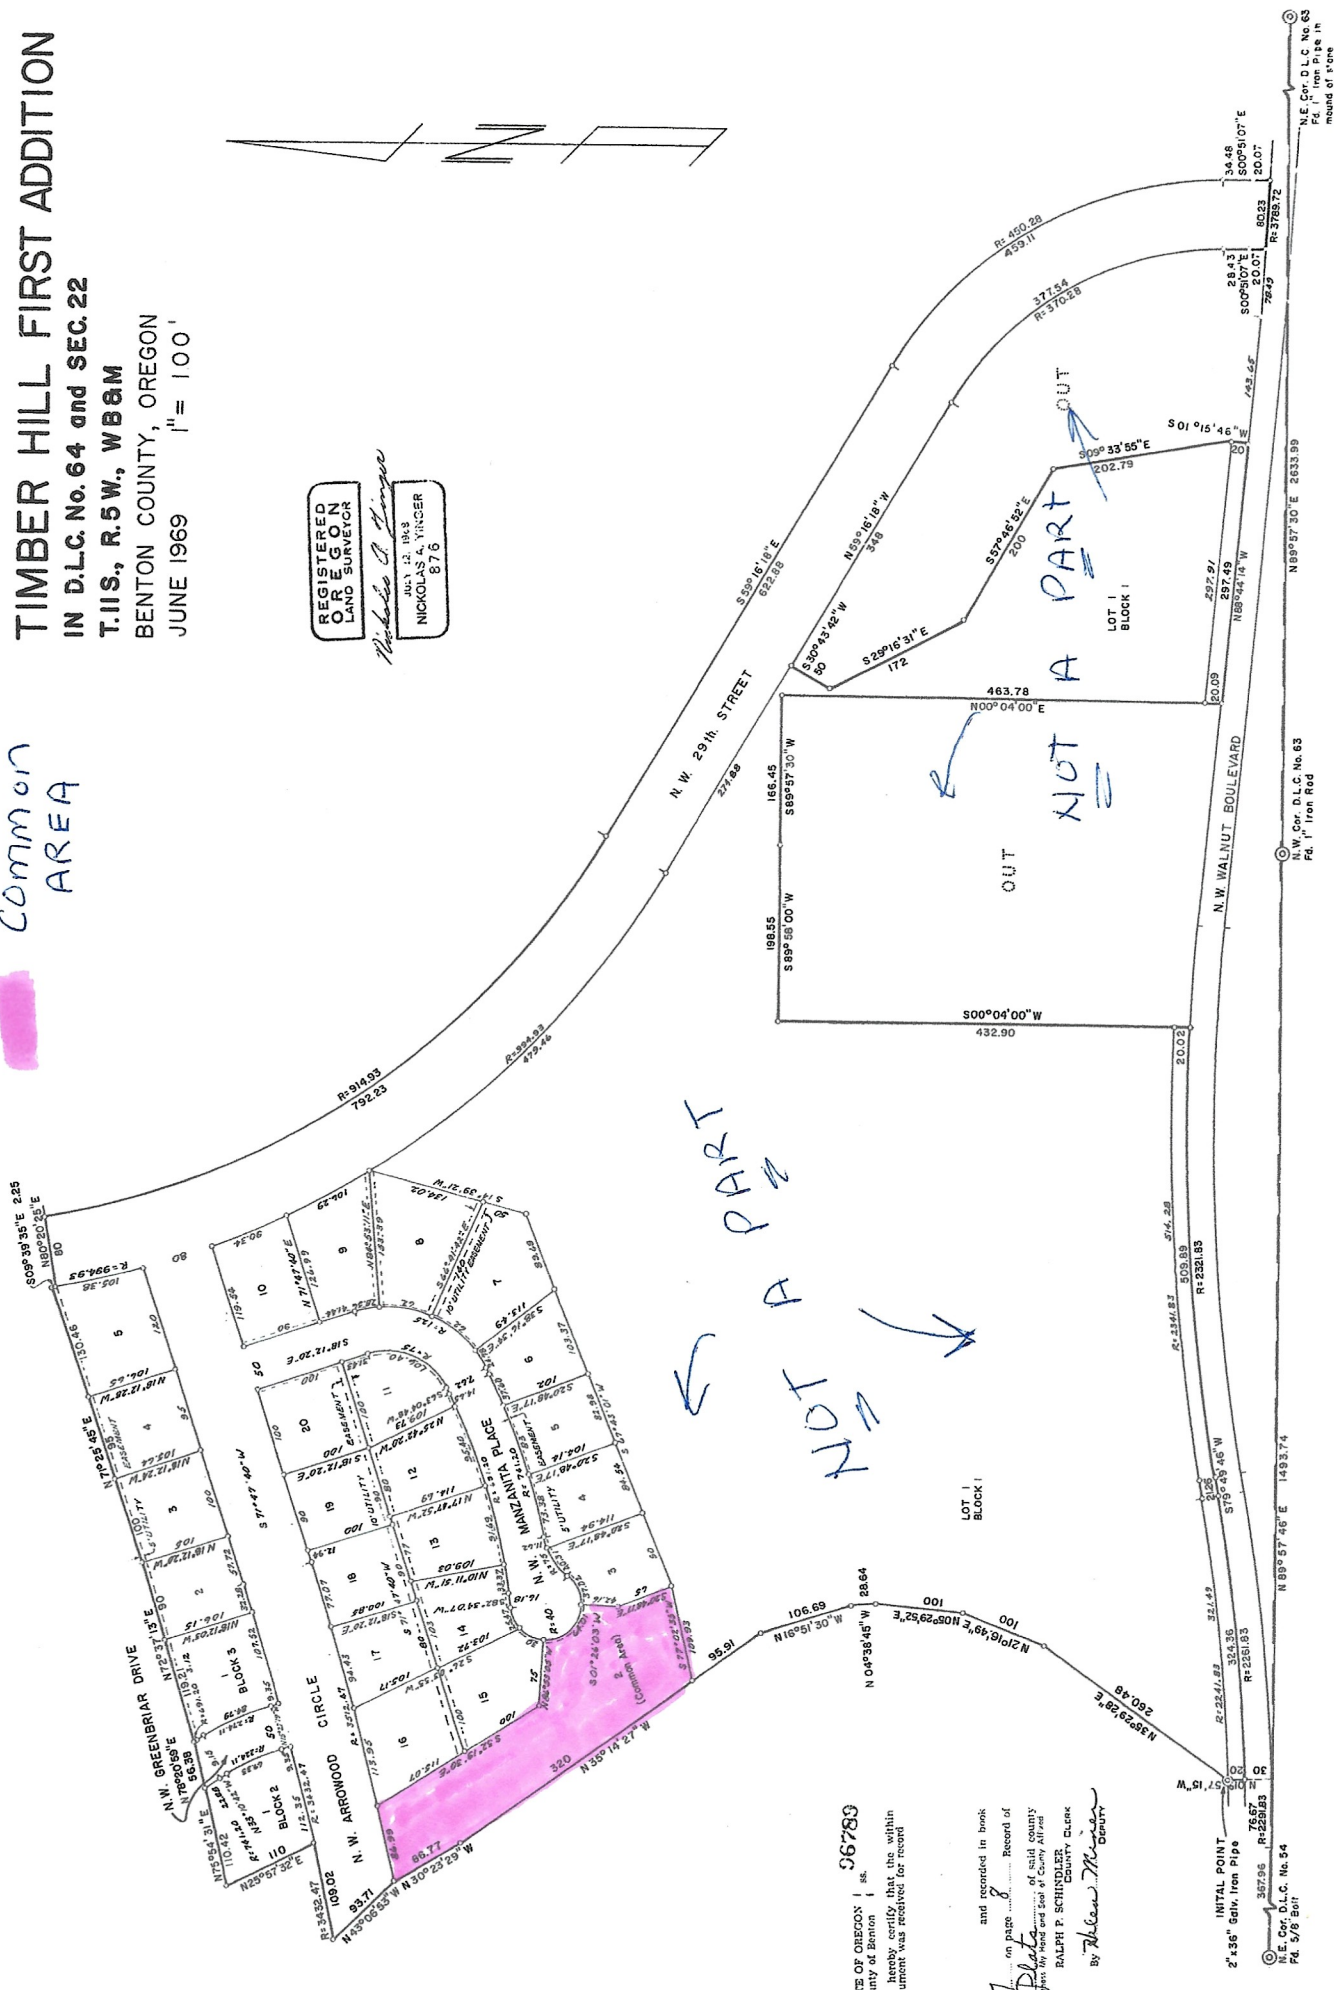

56783
 OF OREGON
 hereby certify that the within
 amount was received for record

and recorded in book
 on page 8
 of said county
 Ralph P. Schindler
 County Clerk
 By *John M. Mearns*
 Deputy

INITIAL POINT
 2' x 36" Galv. Iron Pipe
 25796
 N.E. Cor. D.L.C. No. 64
 Pg. 5/6 5011